HYDE PARK
DEVELOPMENTS

mimar

EGY SMART
FOR MODERN ENGINEERING

Hyde Park North Project

REQUEST FOR INSPECTION AND APPROVAL

CONTRACT NAME : **Remaining finishes work (part A)**
Contract No. : -CP48
ARCH

CONTRACTOR : Egysmart for Modern Engineering
Request No. SS-CP48-IR-ARCH-**0001**

CLUSTER NO.: TH-75
Rev. No. : **0**

DATE.:
Previous Request No. :

TO: Mimar Egypt Engineering Consultants

The following items are ready for your inspection on (Date): 2026-04-29 at (time): 2.00PM

LOCATION: TH-75 LEVEL: AXIS:

DRAWING REF: 2493-TH-AE101-B13-8-AE101
2493-TH-AE102-B13-8-AE102
Activity ID: Architectural Work

Description:

Preparation of spatter dash coat, plaster dots and axes setting out at Ground & First Floors TH-75.

EGYSMART
FOR MODERN ENGINEERING
ايجي سمارت للهندسة الحديثة

EGYSMART
FOR MODERN ENGINEERING
2/5/2026
RECEIVED

SURVEY____ STRUCTURE____ ARCHITECTURE____ MECHANICAIL____ ELECTRICAIL____

All requests must be submitted at least 24 hours prior to the required inspection and approval.

Site Engine : (Contractor)
QA/QC Engineer : (Contractor)
Project Manager : (Contractor)

Received Date ____ Time ____ Engineer's Signature ____

Engineer's Approval / Comments: Code A - Approved ☐ Code B - Approved with comments ☑ Code C - Rejected & Resubmit ☐

* Rectify dots indicated on site
* adjust void parts at spatter dash Coat
* surface preparation to be done
* Consider curing for work

Received
29 APR 2026
mimar
Architecture & Engineering

Engineer's Signature ____ Date: 29-4-2026

Contractor's Received Date ____ Time ____ Contractor's Rep. ____

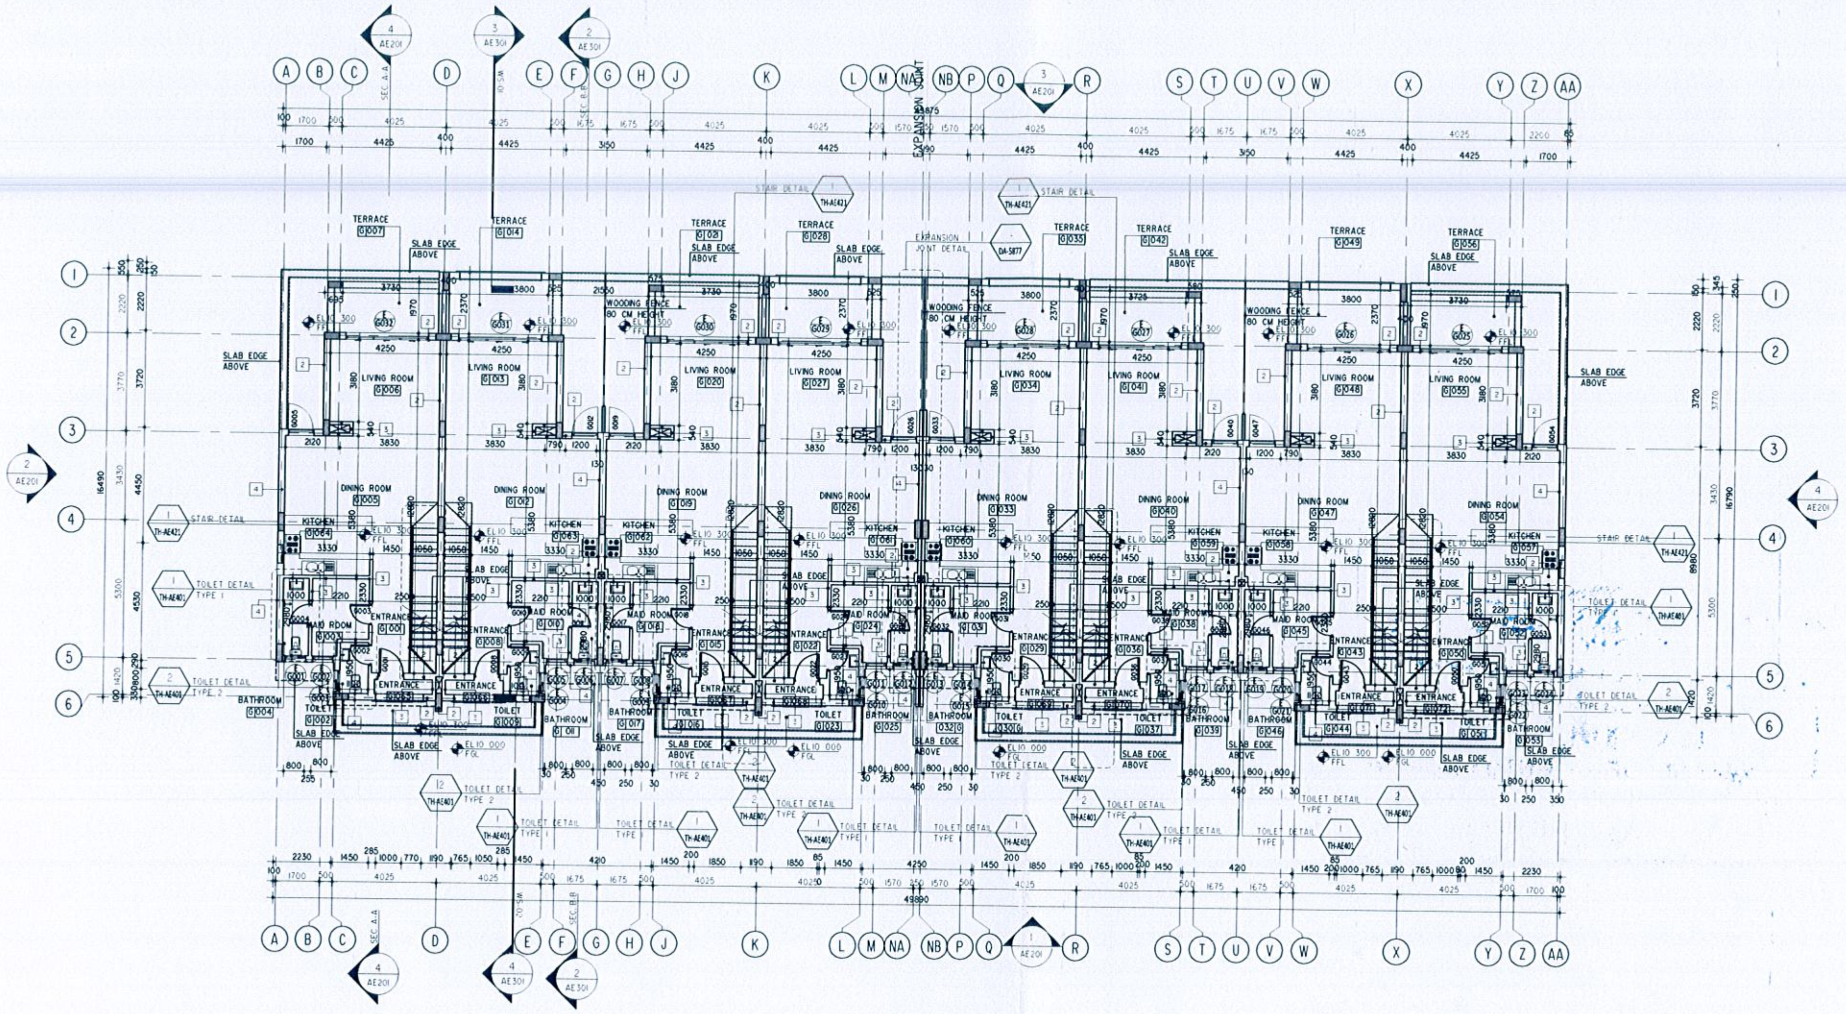

1 GROUND FLOOR PLAN
1:100

CLIENT:

HYDE PARK PROPERTIES FOR DEVELOPMENT

HYDE PARK DEVELOPMENTS

LEAD CONSULTANT:

ECG جماعة المهندسين الاستشاريين
ENGINEERING CONSULTANTS GROUP S.A.
www.ecgsa.com

REMARKS:

- ALL DIMENSIONS ARE METRIC (IN mm.)
- FGL = FIXED GROUND LEVEL = 10 000
- FFL = FINISHED FLOOR LEVEL.
- TOC = TOP OF CONCRETE.
- FPL = FINISHED PAVEMENT LEVEL.
- FRL = FINISHED ROAD LEVEL.
- TOPR = TOP OF PARAPET.

NOTES:

- ALL DIMENSIONS SHOULD BE VERIFIED ON SITE AND APPROVED BY THE AUTHORIZED ENGINEER.
- UNLESS OTHERWISE INDICATED, DIMENSIONS ARE IN MILLIMETERS AND ANGLES ARE IN DEGREES.
- DRAWINGS ARE NOT TO BE SCALED, WRITTEN DIMENSIONS SHOULD BE FOLLOWED.
- ALL DRAWINGS SHOULD BE READ IN CONJUNCTION WITH OTHER RELEVANT ARCHITECTURAL, STRUCTURAL, MECHANICAL, ELECTRICAL DRAWINGS AND ALL OTHER RELEVANT SECTIONS OF SPECIFICATIONS.
- FOR SYMBOLS & ABBREVIATIONS, REFER TO DRAWING A1002.
- FOR STRUCTURE ELEMENTS AND STRUCTURE ELEMENTS SUPPORTING MASONRY WORKS REFER TO STRUCTURAL DRAWINGS.
- UNLESS OTHERWISE INDICATED, ALL THE STRUCTURE ELEMENTS SUPPORTING MASONRY WALLS SHOULD BE WITHIN WALLS THICKNESS.
- FOR EXTERNAL LEVELS, SLOPES, FINISHES, DIMENSIONS, ETC..., REFER TO LANDSCAPE & ROADS DRAWINGS.
- FOR DOORS, WINDOWS AND ELEVATION TYPES' LOCATION AND DIMENSIONS REFER TO OPENINGS TYPE SHEETS AND SCHEDULES.
- JUNCTIONS BETWEEN REINFORCED CONCRETE AND BLOCK WORKS SHOULD BE TREATED BY METAL LATH PRIOR TO APPLYING PLASTER.
- ALL KITCHEN AND TOILETS WALLS SHOULD BE OF SOLID MASONRY UNITS.
- UNLESS OTHERWISE INDICATED ON DRAWINGS, DOOR JAMBS SHOULD BE LOCATED 200mm FROM THE NEAREST ADJACENT WALL FACE.
- FOR EXACT LOCATION AND SIZE OF MEP OPENINGS, REFER TO STRUCTURAL DRAWINGS. SHOP DRAWINGS FOR THE COORDINATED OPENINGS SHOULD BE SUBMITTED TO THE AUTHORIZED ENGINEER FOR APPROVAL.
- ALL WALL SHOULDERS BEHIND ALL DOORS ARE EQUAL 120MM
- ALL MECH. SHAFTS ARE ACCESSIBLE BY ACCESS PANEL IN THE TOILETS AS PER STANDARD DETAIL NO. DA-8108-A

WALL TYPES:

W01	CONC. HOLLOW BLOCK 120mm THICK.
W02	CONC. HOLLOW BLOCK 250mm THICK.
W03	CONC. SOLID BLOCK 120mm THICK.
W04	CONC. SOLID BLOCK 250mm THICK.

KEY PLAN

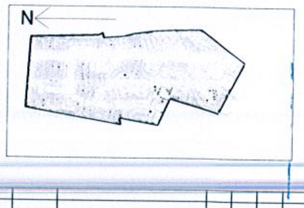

REV	DATE	ISSUED FOR	DRW	CHK	TL	PM
0	OCT-2022	ISSUED FOR CONSTRUCTION	A.HZEB	A.HSGS	A.PMD	A.RGFI

PROJECT DATA:

TOWN HOUSE 8 PLEX
NORTH COAST, EGYPT

DISCIPLINE
ARCHITECTURE

SHEET TYPE
ARCHITECTURAL ELEMENT

SHEET TITLE
GROUND FLOOR PLAN

SCALE	PROJECT NO.	SITE NO/BLDG NO	SHEET NO.	REV.
1:100	2493	B13	AE101	0

A0

THIS DRAWING AND THE DESIGN IT COVERS ARE THE PROPERTY OF THE ENGINEERING CONSULTANTS GROUP. THEY ARE MERELY LOANED ON THE BORROWER'S EXPRESSED AGREEMENT THAT THEY WILL NOT BE REPRODUCED, COPIED, LOANED, EXHIBITED NOR USED EXCEPT FOR LIMITED AND PRIVATE USE PERMITTED BY WRITTEN CONSENT GIVEN BY THE LENDER TO THE BORROWER

PROJECT NO.	BLDG NO.	SHEET NO.
2493	B13	AE102

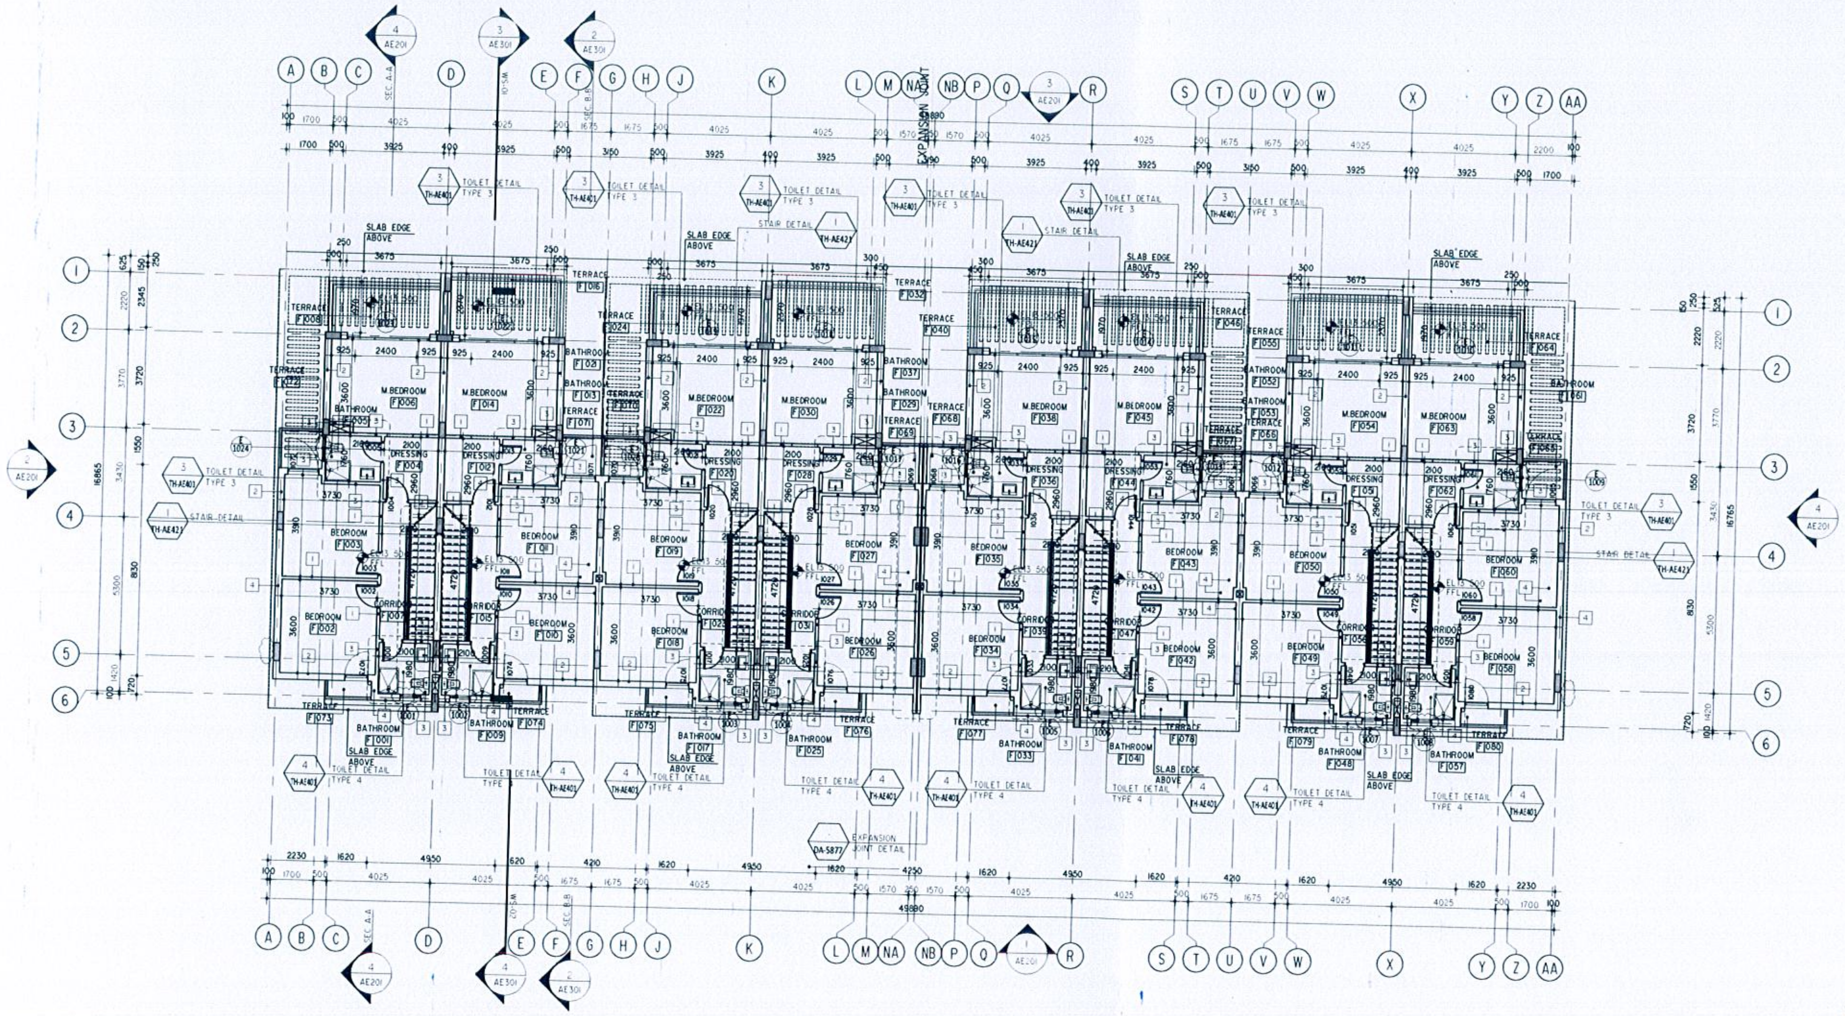

2 FIRST FLOOR PLAN
1:100

CLIENT:

HYDE PARK PROPERTIES
FOR DEVELOPMENT

HYDE PARK
DEVELOPMENTS

LEAD CONSULTANT:

ECG جماعة المهندسين الاستشاريين
ENGINEERING CONSULTANTS GROUP S.A.
www.ecgsa.com

REMARKS:

- ALL DIMENSIONS ARE METRIC (IN mm)
- FGL = FIXED GROUND LEVEL = 10 000
- FFL = FINISHED FLOOR LEVEL.
- TOC = TOP OF CONCRETE.
- FPL = FINISHED PAVEMENT LEVEL.
- FRL = FINISHED ROAD LEVEL.
- TOPR = TOP OF PARAPET.

NOTES:

- ALL DIMENSIONS SHOULD BE VERIFIED ON SITE AND APPROVED BY THE AUTHORIZED ENGINEER.
- UNLESS OTHERWISE INDICATED, DIMENSIONS ARE IN MILLIMETERS AND ANGLES ARE IN DEGREES.
- DRAWINGS ARE NOT TO BE SCALED, WRITTEN DIMENSIONS SHOULD BE FOLLOWED.
- ALL DRAWINGS SHOULD BE READ IN CONJUNCTION WITH OTHER RELEVANT ARCHITECTURAL, STRUCTURAL, MECHANICAL, ELECTRICAL DRAWINGS AND ALL OTHER RELEVANT SECTIONS OF SPECIFICATIONS.
- FOR SYMBOLS & ABBREVIATIONS, REFER TO DRAWING A1002.
- FOR STRUCTURE ELEMENTS AND STRUCTURE ELEMENTS SUPPORTING MASONRY WORKS REFER TO STRUCTURAL DRAWINGS.
- UNLESS OTHERWISE INDICATED, ALL THE STRUCTURE ELEMENTS SUPPORTING MASONRY WALLS SHOULD BE WITHIN WALLS THICKNESS.
- FOR EXTERNAL LEVELS, SLOPES, FINISHES, DIMENSIONS, ETC..., REFER TO LANDSCAPE & ROADS DRAWINGS.
- FOR DOORS, WINDOWS AND ELEVATION TYPES' LOCATION AND DIMENSIONS REFER TO OPENINGS TYPE SHEETS AND SCHEDULES.
- JUNCTIONS BETWEEN REINFORCED CONCRETE AND BLOCK WORKS SHOULD BE TREATED BY METAL LATH PRIOR TO APPLYING PLASTER.
- ALL KITCHEN AND TOILETS WALLS SHOULD BE OF SOLID MASONRY UNITS.
- UNLESS OTHERWISE INDICATED ON DRAWINGS, DOOR JAMBS SHOULD BE LOCATED 200mm FROM THE NEAREST ADJACENT WALL FACE.
- FOR EXACT LOCATION AND SIZE OF MEP OPENINGS, REFER TO STRUCTURAL DRAWINGS. SHOP DRAWINGS FOR THE COORDINATED OPENINGS SHOULD BE SUBMITTED TO THE AUTHORIZED ENGINEER FOR APPROVAL.
- ALL WALL SHOULDERS BEHIND ALL DOORS ARE EQUAL 120MM
- ALL MECH. SHAFTS ARE ACCESSIBLE BY ACCESS PANEL IN THE TOILETS AS PER STANDARD DETAIL NO. DA-B108-A

WALL TYPES:

W01	CONC. HOLLOW BLOCK 120mm THICK.
W02	CONC. HOLLOW BLOCK 250mm THICK.
W03	CONC. SOLID BLOCK 120mm THICK.
W04	CONC. SOLID BLOCK 250mm THICK.

KEY PLAN:

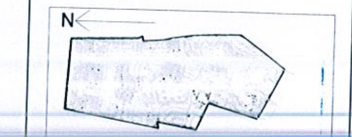

REV	DATE	ISSUED FOR	DRW	CHK	TL	PM
0	OCT-2022	ISSUED FOR CONSTRUCTION	A.HZEB	A.HSGS	A.RMD	A.RGFI

PROJECT DATA:

TOWN HOUSE 8 PLEX
NORTH COAST, EGYPT

DISCIPLINE
ARCHITECTURE

SHEET TYPE
ARCHITECTURAL ELEMENT

SHEET TITLE
FIRST FLOOR PLAN

SCALE	PROJECT NO.	SITE NO/BLDG NO	SHEET NO.	REV.
1:100	2493	B13	AE102	0

A0

Scanning scale 10 mm 50 mm

THIS DRAWING AND THE DESIGN IT COVERS ARE THE PROPERTY OF THE ENGINEERING CONSULTANTS GROUP. THEY ARE MERELY LOANED ON THE BORROWER'S EXPRESSED AGREEMENT THAT THEY WILL NOT BE REPRODUCED, COPIED, LOANED, EXHIBITED NOR USED EXCEPT FOR LIMITED AND PRIVATE USE PERMITTED BY WRITTEN CONSENT GIVEN BY THE LENDER TO THE BORROWER.