EGYSMART
FOR MODERN ENGINEERING
إيجي سمارت للهندسة الحديثة

HYDE PARK
DEVELOPMENTS

mimar

EGY SMART
FOR MODERN ENGINEERING

Hyde Park North Project

REQUEST FOR INSPECTION AND APPROVAL

CONTRACT NAME : **Remaining finishes work (part A)**
Contract No. : -CP48
MECH
CONTRACTOR : Egysmart for Modern Engineering
Request No. SS-CP48-IR-ELEC-**0001**
CLUSTER NO.: TH-71
Rev. No. : **0**
DATE.:
Previous Request No. :
TO: Mimar Egypt Engineering Consultants

The following items are ready for your inspection on (Date): 2026-06-17 at (time): 2.00PM
LOCATION: TH-71
LEVEL:
AXIS:
DRAWING REF: N-CP07-SD-E-0027
Activity ID: ELECTRICAIL Work

EGYSMART
FOR MODERN ENGINEERING
25/6/2026
RECEIVED

Description:

Electrical power conduits installation under Slab on Grade (SOG) FOR TH-71

SURVEY ____ STRUCTURE ____ ARCHITECTURE ____ MECHANICAL ____ ELECTRICAIL ____

All requests must be submitted at least 24 hours prior to the required inspection and approval.

Site Engineer: (Contractor)
QA/QC Engineer : (Contractor)
Project Manager : (Contractor)

Received Date ____
Time ____
Engineer's Signature ____

Engineer's Approval / Comments:
Code A - Approved ☐
Code B - Approved with comments ☑
Code C - Rejected & Resubmit ☐

Protection of work are under Contractor responsibility

Engineer's Signature ____
Date: 23/6/2026

Received
10 JUN 2026
mimar
Architecture & Engineering

Contractor's Received Date ____
Time ____
Contractor's Rep. ____

PROJECT NO.	BLDG NO.	SHEET NO.
2493	B13	MODEL

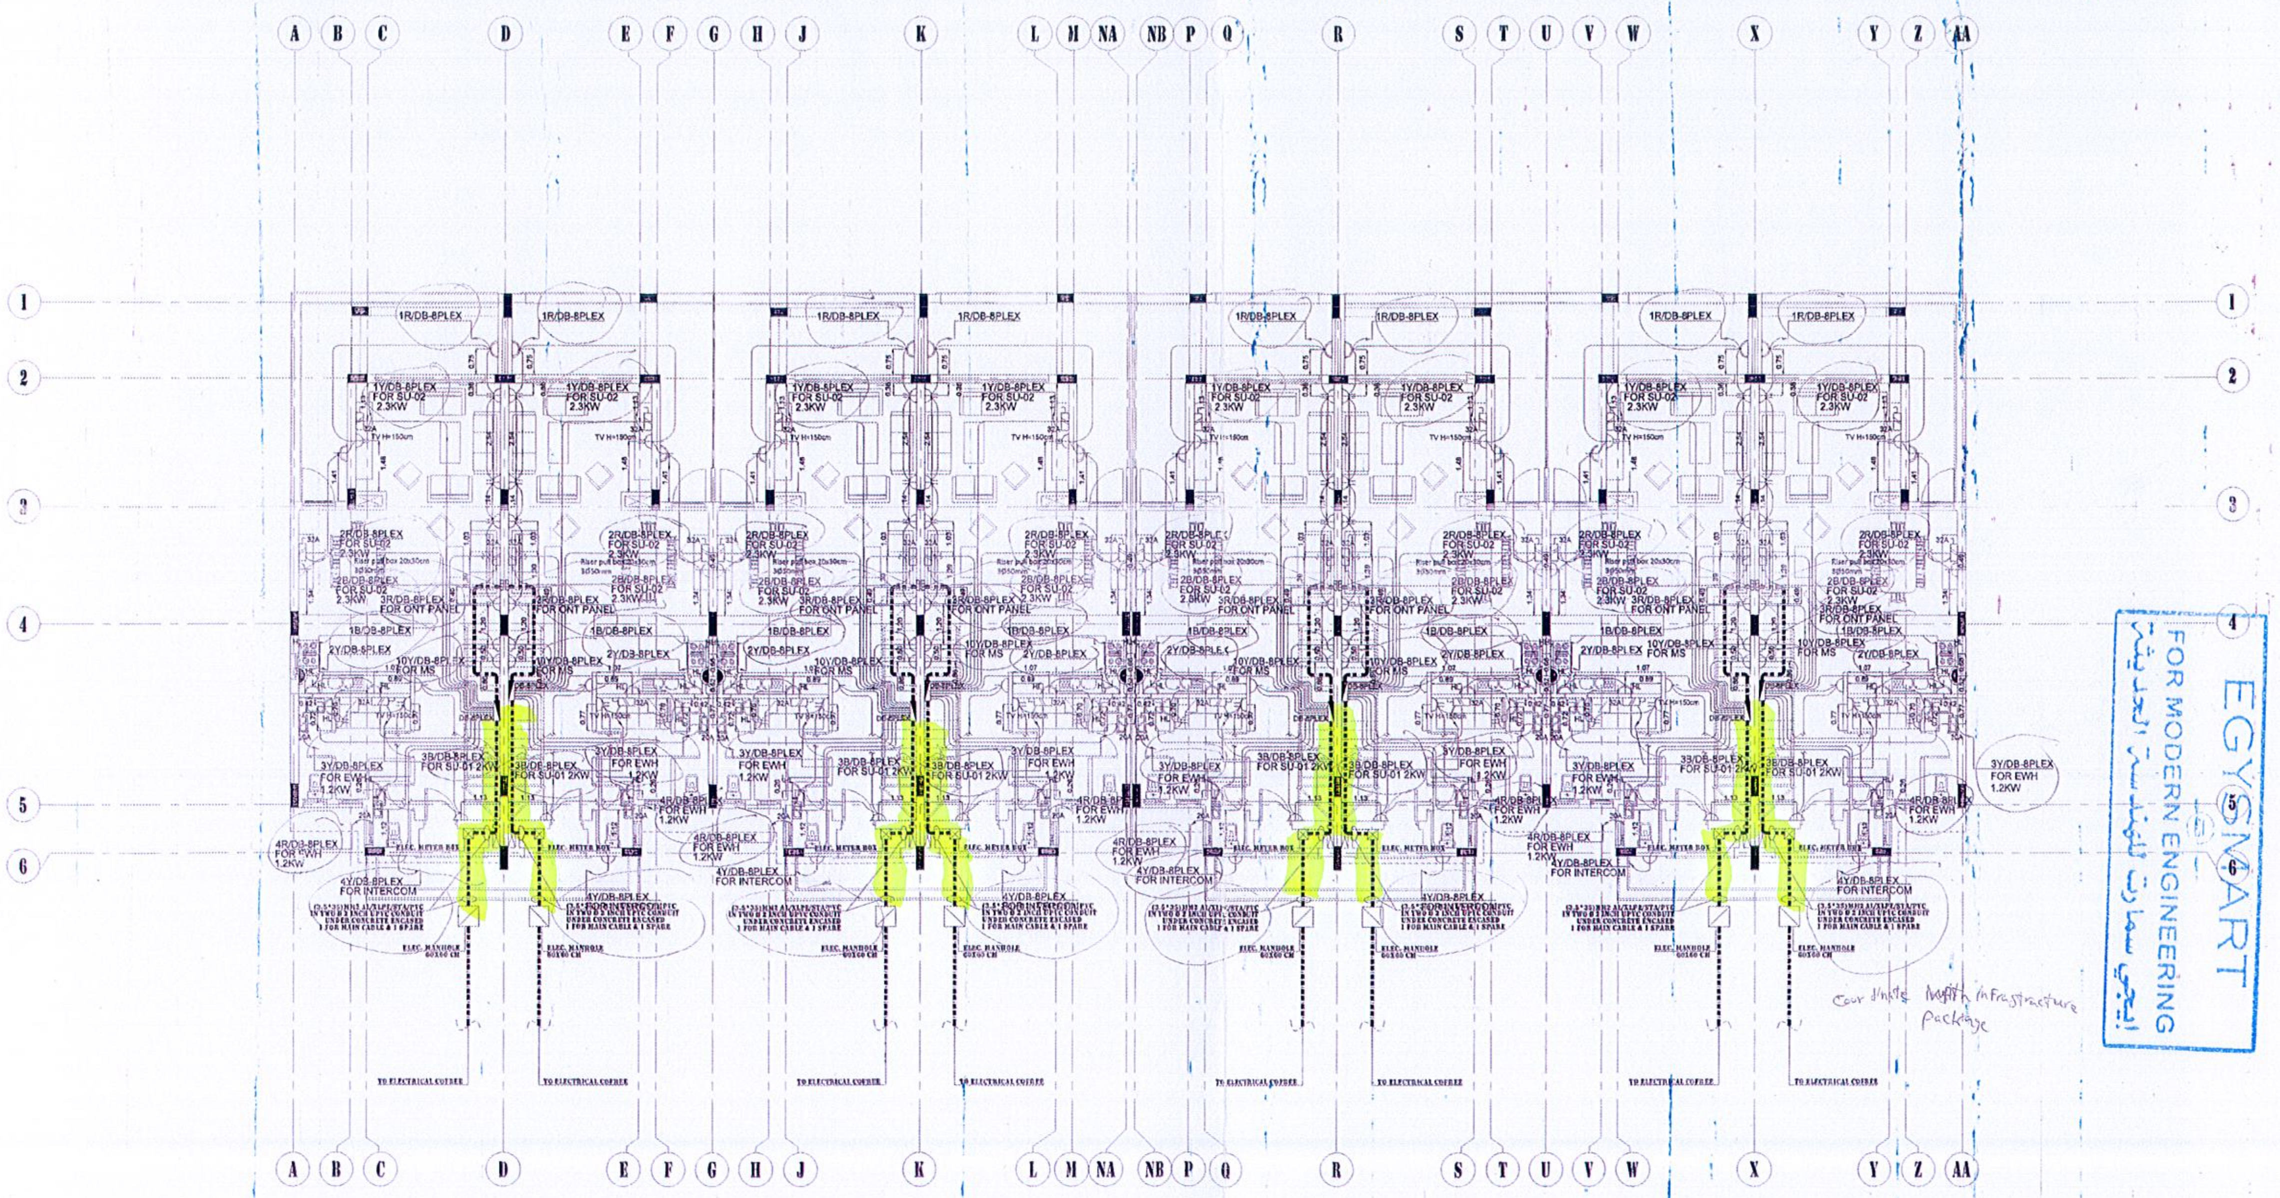

Coordinate with infrastructure package

EGYSMART
FOR MODERN ENGINEERING
ايجي سمارت للهندسة الحديثة

missing
* conduit dimension
* no of wires, dimension for wires
* consists of each circuit (phase, neutral, earth, return)

1 GROUND FLOOR PLAN

CLIENT:

HYDE PARK PROPERTIES
FOR DEVELOPMENT

HYDE PARK
DEVELOPMENTS

LEAD CONSULTANT:

mimar

Mimar Group
@mimargroup.consultant
Engineering service

SMALL POWER SYSTEM LEGEND :-

REMARKS	SYMBOLS	DESCRIPTION
S01	△	220V-13A, CONVENIENCE SOCKET OUTLET, 2P+E, IP20 FLUSH MOUNTED WITH SAFETY SHUTTERS, AND SIDE EARTH CONTACT (SCHUKO TYPE). (EMPTY CONDUIT ONLY)
S02	△	SAME AS S01 BUT DUPLEX TYPE. (EMPTY CONDUIT ONLY)
S03	△	SAME AS S01 BUT WEATHER PROOF TYPE, IP54, (EMPTY CONDUIT ONLY)
S04	△	220V-16A, CONVENIENCE TWIN SOCKET OUTLETS, 2P+E, IP20 MOUNTED AT RIGHT LEVEL FOR TV OUTLET, WITH SAFETY SHUTTERS, AND SIDE EARTH CONTACT (SCHUKO TYPE). (MOUNTING HEIGHT MUST BE COORDINATED WITH ID PLANS). (EMPTY CONDUIT ONLY)
S05	▲	POWER SOCKET OUTLET, 16A, 220V, WITH PLUG, IP44, MOUNTED AT LEVEL 1.2 M FROM FFL (EMPTY CONDUIT ONLY)
S06	△	SAME AS S03 BUT MOUNTED AT LEVEL 1.2 m FROM FFL (EMPTY CONDUIT ONLY)
S07	☒	220V-13A, CONVENIENCE SOCKET OUTLET, 2P+E, IP44 FLUSH MOUNTED WITH SAFETY SHUTTERS, AND SIDE EARTH CONTACT (SCHUKO TYPE).
S08	△	ELECTRICAL OUTLET, 16A, 220V, IP55 (EMPTY CONDUIT ONLY)
S09	△	SAME AS S02 BUT BUT WEATHER PROOF TYPE, IP54, (EMPTY CONDUIT ONLY)
	☒	ELEC. METER BOX
	▨	ELEC. MANHOLE
SMDB	▬	SUB MAIN ELECTRICAL DISTRIBUTION BOARD
DB	▬	ELECTRICAL DISTRIBUTION BOARD (FLUSH MOUNTED)
G01	☐	220V, 50Hz, WITH 2P+E DISCONNECT SWITCH OUTLET IP-55, RATING AS INDICATED (EMPTY CONDUIT ONLY)
G02	☐	220V, 50Hz, WITH 2P+E DISCONNECT SWITCH OUTLET IP-54, RATING AS INDICATED (EMPTY CONDUIT ONLY)
G03	☐	380V, 50Hz, WITH 3P+E DISCONNECT SWITCH OUTLET IP-54, RATING AS INDICATED (EMPTY CONDUIT ONLY)

- GENERAL SOCKET OUTLET : 300MM A.F.F.L
- SOCKET AT KITCHEN : GENERAL PURPOSE SOCKETS 1200MM (ABOVE COUNTER),
  - APPLIANCES SOCKETS 600 MM.
- ISOLATOR SWITCH : ADJACENT TO EQUIPMENT

KEY PLAN

REV	DATE	ISSUED FOR	DRW	CHK	TL	PM
0	OCT-2022	CONSTRUCTION	[illegible]	[illegible]	[illegible]	[illegible]

PROJECT DATA:

TOWN HOUSE 8 PLEX
NORTH COAST, EGYPT

DISCIPLINE
ELECTRICAL

SHEET TYPE
POWER LAYOUT SHOPDRAWING

SHEET TITLE
GROUND FLOOR PLAN
N-CP07-B08-E-P-GR-042

SCALE	PROJECT NO.	SITE NO/BLDG NO	SHEET NO.	REV.
1:50	2493	B08	MODEL	0

THIS DRAWING AND THE DESIGN IT COVERS ARE THE PROPERTY OF THE ENGINEERING CONSULTANTS GROUP. THEY ARE MERELY LOANED ON THE BORROWER'S EXPRESSED AGREEMENT THAT THEY WILL NOT BE REPRODUCED, COPIED, LOANED, EXHIBITED NOR USED EXCEPT FOR LIMITED AND PRIVATE USE PERMITTED BY WRITTEN CONSENT GIVEN BY THE LENDER TO THE BORROWER.